Третий этаж



Ведомость площадей 3 этаж

п/п	Наименование	Площадь полезная	Площадь балконов	Площадь общая
1	Апартамент № 313	26,56	9,4	35,96
1А	Апартамент № 314	61,37	11,60	72,97
2	Апартамент № 315	37,33	7,10	44,43
3	Апартамент № 316	53,84	8,2	62,04
4	Апартамент № 317	65,61	8,2	73,81
5	Апартамент № 318	27,27	8,2	35,47
6	Апартамент № 319	27,27	8,2	35,47
7	Апартамент № 320	27,27	8,2	35,47
8	Апартамент № 321	27,27	8,2	35,47
9	Апартамент № 322	27,27	8,2	35,47
10	Апартамент № 323	27,27	8,2	35,47
11	Апартамент № 324	41,83	14,60	56,43
12	Апартамент № 325	58,2	18,53	76,73
13	Апартамент № 326	25,98	6,88	32,86
14	Апартамент № 327	25,98	6,88	32,86
15	Апартамент № 328	25,98	6,88	32,86
	Итого	586,3	147,47	733,77
А	Коридор	80,52		
Б	Лифт, лестничный марш	24,49		
В	Служебное помещение	4,0		
Г	Лифт, лестничный марш	24,19		
	ИТОГО	719,5	147,47	866,97


1 комнатные

2-х комнатные

3. Третий этаж 1:180

Изм.	Кол.уч.	Лист	№Док.	Подпись	Дата	Гостиница РА г.Гагра ул.Морская. 6 "Alex Apartaments Resort & SPA"	Стадия	Лист	Масштаб
							АР	04.4	1:180
Выполнил		Лобанов В.А.			11.10.2022	Третий этаж	ООО		
ГИП									

Четвертый этаж

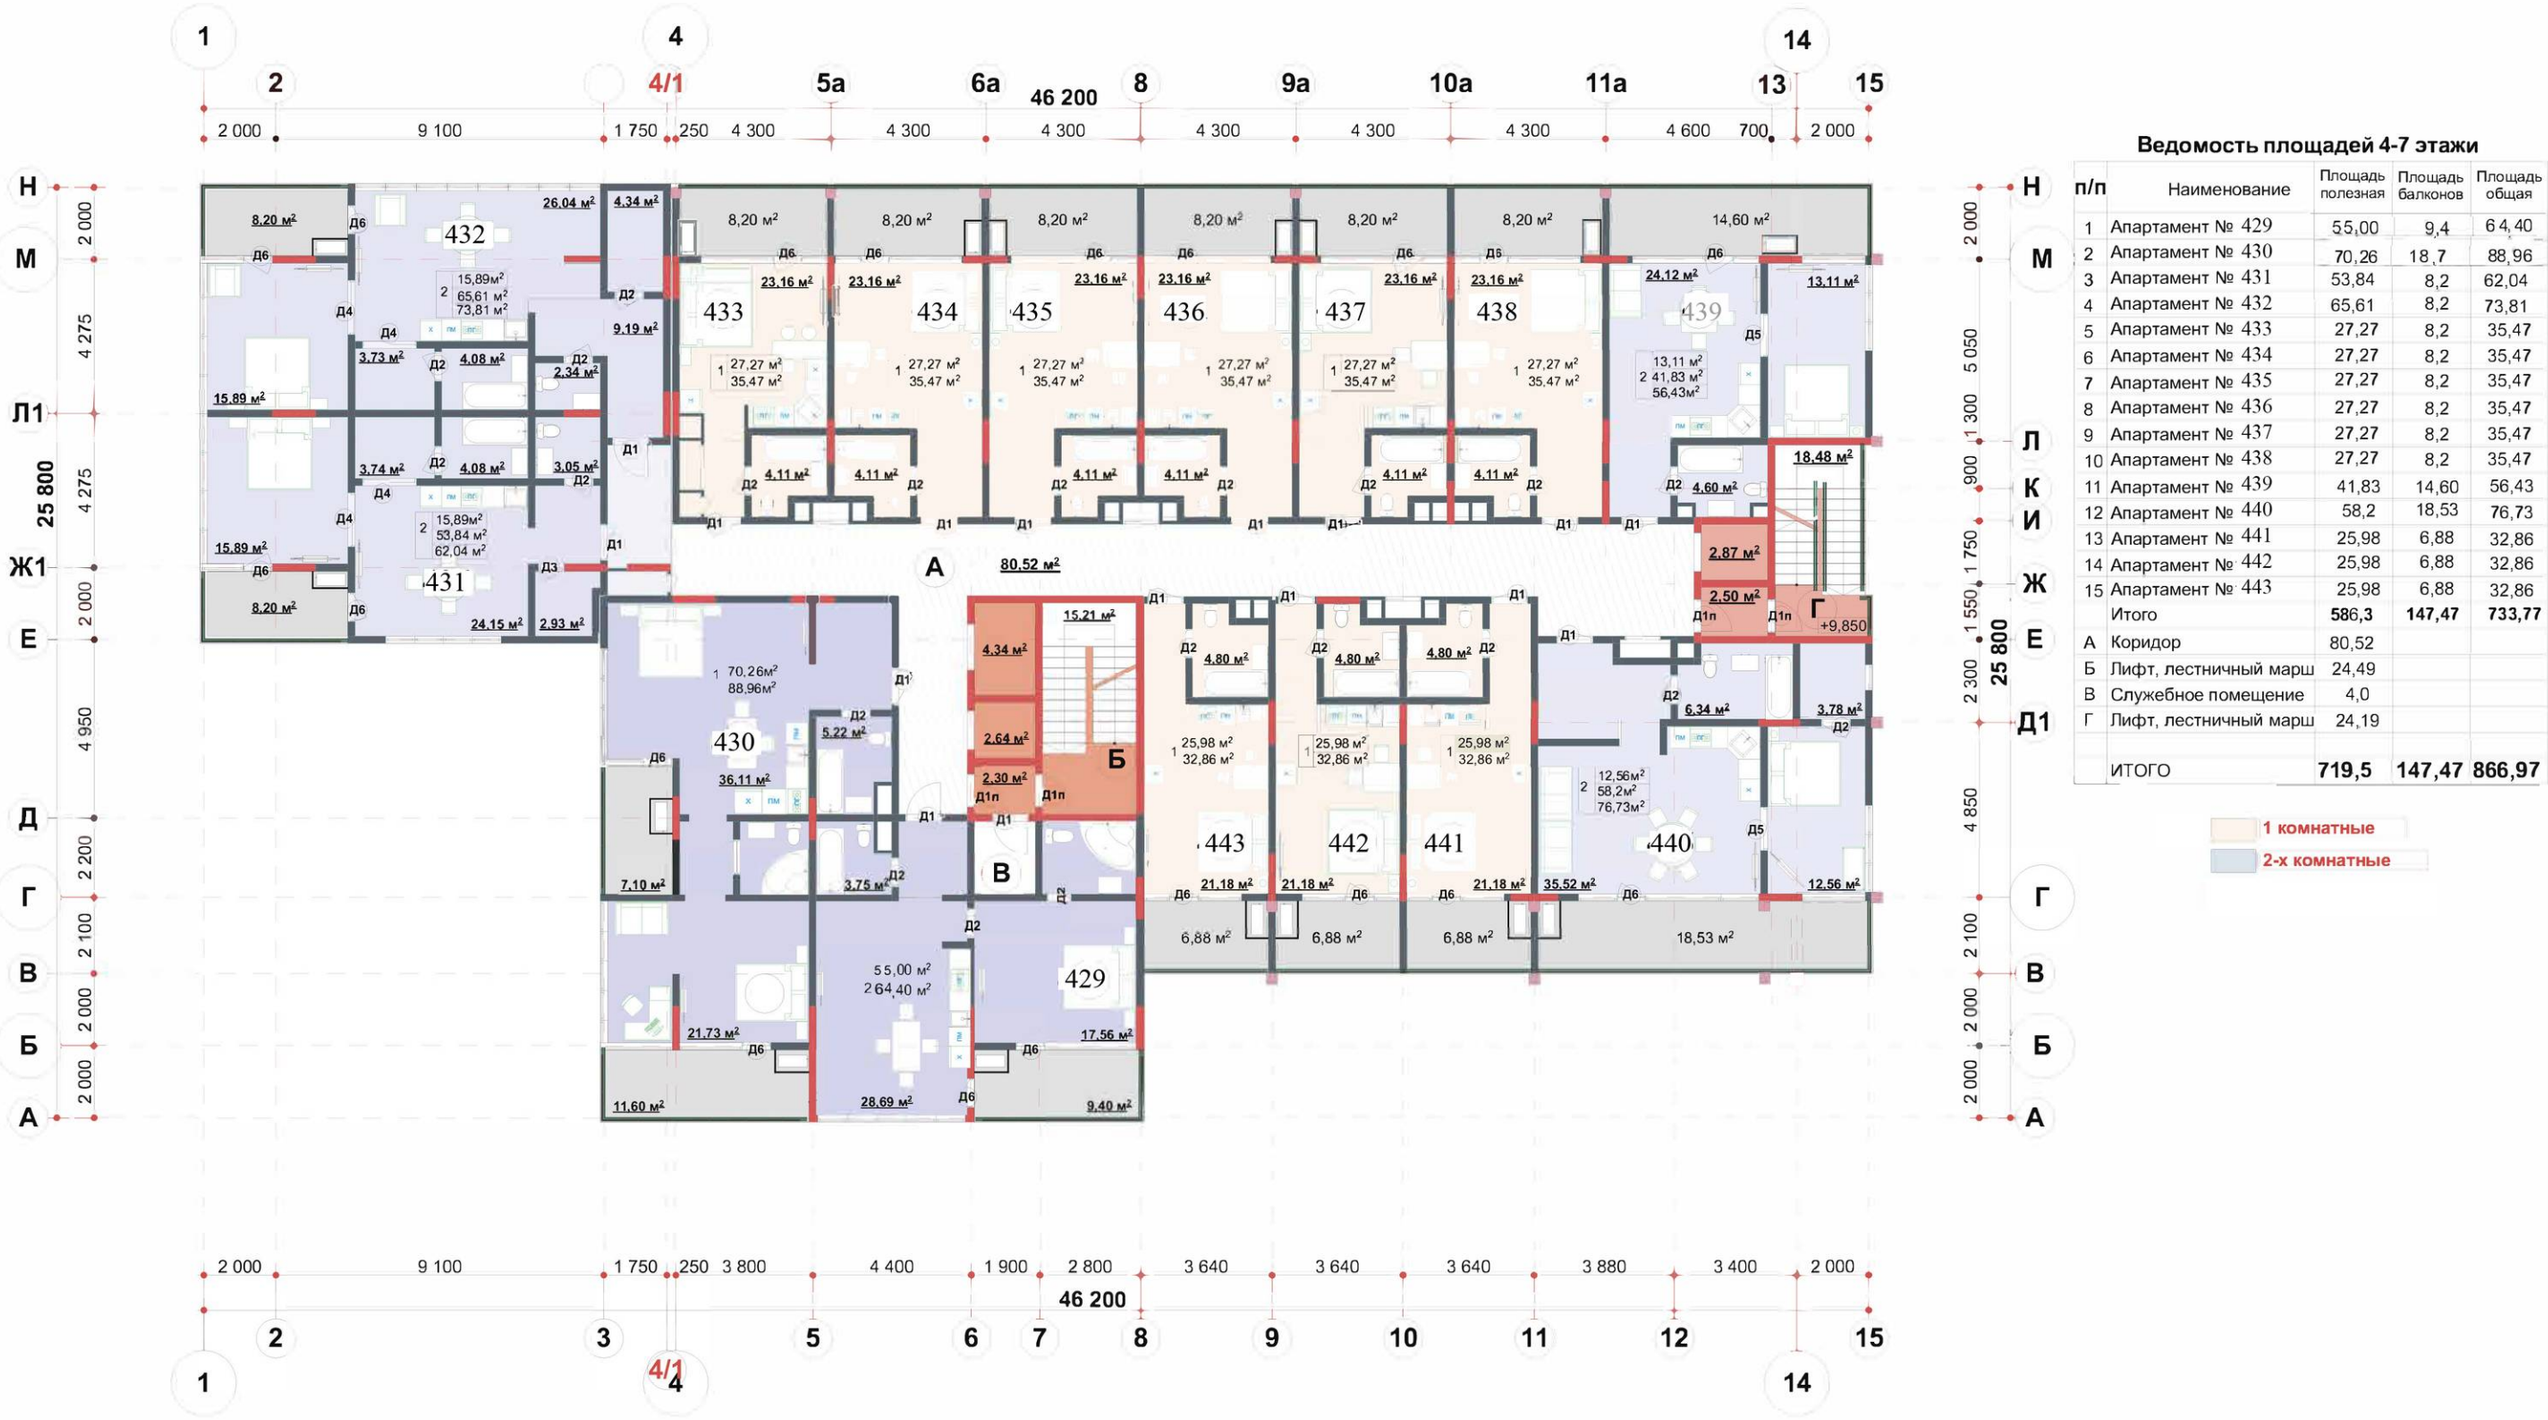

Ведомость площадей 4-7 этажи

п/п	Наименование	Площадь полезная	Площадь балконов	Площадь общая
1	Апартамент № 429	55,00	9,4	64,40
2	Апартамент № 430	70,26	18,7	88,96
3	Апартамент № 431	53,84	8,2	62,04
4	Апартамент № 432	65,61	8,2	73,81
5	Апартамент № 433	27,27	8,2	35,47
6	Апартамент № 434	27,27	8,2	35,47
7	Апартамент № 435	27,27	8,2	35,47
8	Апартамент № 436	27,27	8,2	35,47
9	Апартамент № 437	27,27	8,2	35,47
10	Апартамент № 438	27,27	8,2	35,47
11	Апартамент № 439	41,83	14,60	56,43
12	Апартамент № 440	58,2	18,53	76,73
13	Апартамент № 441	25,98	6,88	32,86
14	Апартамент № 442	25,98	6,88	32,86
15	Апартамент № 443	25,98	6,88	32,86
	Итого	586,3	147,47	733,77
А	Коридор	80,52		
Б	Лифт, лестничный марш	24,49		
В	Служебное помещение	4,0		
Г	Лифт, лестничный марш	24,19		
	ИТОГО	719,5	147,47	866,97

1 комнатные

2-х комнатные

4. Четвертый этаж 1:180

Изм.	Кол.уч.	Лист	№Док.	Подпись	Дата	Гостиница РА г.Гагра ул.Морская. 6 "Alex Apartaments Resort & SPA"	Стадия	Лист	Масштаб
							АР	04.5	1:180
Выполнил		Лобанов В.А.			11.10.2022	Четвертый этаж	ООО		
ГИП									

Пятый этаж



Ведомость площадей 4-7 этажи

п/п	Наименование	Площадь полезная	Площадь балконов	Площадь общая
1	Апартамент №544	55,00	9,4	64,40
2	Апартамент №545	70,26	18,7	88,96
3	Апартамент №546	53,84	8,2	62,04
4	Апартамент №547	65,61	8,2	73,81
5	Апартамент №548	27,27	8,2	35,47
6	Апартамент №549	27,27	8,2	35,47
7	Апартамент №550	27,27	8,2	35,47
8	Апартамент №551	27,27	8,2	35,47
9	Апартамент №552	27,27	8,2	35,47
10	Апартамент №553	27,27	8,2	35,47
11	Апартамент №554	41,83	14,60	56,43
12	Апартамент №555	58,2	18,53	76,73
13	Апартамент №556	25,98	6,88	32,86
14	Апартамент №557	25,98	6,88	32,86
15	Апартамент №558	25,98	6,88	32,86
	Итого	**586,3**	**147,47**	**733,77**
А	Коридор	80,52		
Б	Лифт, лестничный марш	24,49		
В	Служебное помещение	4,0		
Г	Лифт, лестничный марш	24,19		
	ИТОГО	**719,5**	**147,47**	**866,97**

1 комнатные
2-х комнатные

2 000 9 100 1 750 250 3 800 4 400 1 900 2 800 3 640 3 640 3 640 3 880 3 400 2 000
46 200
1 2 3 4/1 5 6 7 8 9 10 11 12 14 15

5. Пятый этаж 1:180

Изм.	Кол.уч.	Лист	№Док.	Подпись	Дата	Гостиница РА г.Гагра ул.Морская. 6 "Alex Apartaments Resort & SPA"	Стадия	Лист	Масштаб
							АР	04.6	1:180
Выполнил		Любанов В.А.			11.10.2022	Пятый этаж	ООО		
ГИП									

Шестой этаж



Ведомость площадей 4-7 этажи

п/п	Наименование	Площадь полезная	Площадь балконов	Площадь общая
1	Апартамент №659	55,00	9,4	64,40
2	Апартамент №660	70,26	18,7	88,96
3	Апартамент №661	53,84	8,2	62,04
4	Апартамент №662	65,61	8,2	73,81
5	Апартамент №663	27,27	8,2	35,47
6	Апартамент №664	27,27	8,2	35,47
7	Апартамент №665	27,27	8,2	35,47
8	Апартамент №666	27,27	8,2	35,47
9	Апартамент №667	27,27	8,2	35,47
10	Апартамент №668	27,27	8,2	35,47
11	Апартамент №669	41,83	14,60	56,43
12	Апартамент №670	58,2	18,53	76,73
13	Апартамент №671	25,98	6,88	32,86
14	Апартамент №672	25,98	6,88	32,86
15	Апартамент №673	25,98	6,88	32,86
	Итого	586,3	147,47	733,77
А	Коридор	80,52		
Б	Лифт, лестничный марш	24,49		
В	Служебное помещение	4,0		
Г	Лифт, лестничный марш	24,19		
	ИТОГО	719,5	147,47	866,97

1 комнатные

2-х комнатные

6. Шестой этаж 1:180

Изм.	Кол.уч.	Лист	№Док.	Подпись	Дата	Гостиница РА г.Гагра ул.Морская. 6 "Alex Apartaments Resort & SPA"	Стадия	Лист	Масштаб
							АР	04.7	1:180
Выполнил	Любанов В.А.				11.10.2022	Шестой этаж	ООО		
ГИП									

Седьмой этаж



Ведомость площадей 4-/ этаж

п/п	Наименование	Площадь полезная	Площадь балконов	Площадь общая
1	Апартамент № 774	55,00	9,4	64,40
2	Апартамент № 775	70,26	18,7	88,96
3	Апартамент № 776	53,84	8,2	62,04
4	Апартамент № 777	65,61	8,2	73,81
5	Апартамент № 778	27,27	8,2	35,47
6	Апартамент № 779	27,27	8,2	35,47
7	Апартамент № 780	27,27	8,2	35,47
8	Апартамент № 781	27,27	8,2	35,47
9	Апартамент № 782	27,27	8,2	35,47
10	Апартамент № 783	27,27	8,2	35,47
11	Апартамент № 784	41,83	14,60	56,43
12	Апартамент № 785	58,2	18,53	76,73
13	Апартамент № 786	25,98	6,88	32,86
14	Апартамент № 787	25,98	6,88	32,86
15	Апартамент № 788	25,98	6,88	32,86
	Итого	586,3	147,47	733,77
А	Коридор	80,52		
Б	Лифт, лестничный марш	24,49		
В	Служебное помещение	4,0		
Г	Лифт, лестничный марш	24,19		
	ИТОГО	719,5	147,47	866,97

1 комнатные

2-х комнатные

7. Седьмой этаж 1:180

Изм.	Кол.уч.	Лист	№Док.	Подпись	Дата	Гостиница РА г.Гагра ул.Морская. 6 "Alex Apartaments Resort & SPA"	Стадия	Лист	Масштаб
							АР	04.8	1:180
Выполнил		Лобанов В.А.			24.11.2022	Седьмой этаж Корректировка 21 11 2022 г.	ИП Романов Алексей Иванович mayaksev@mail.ru		